


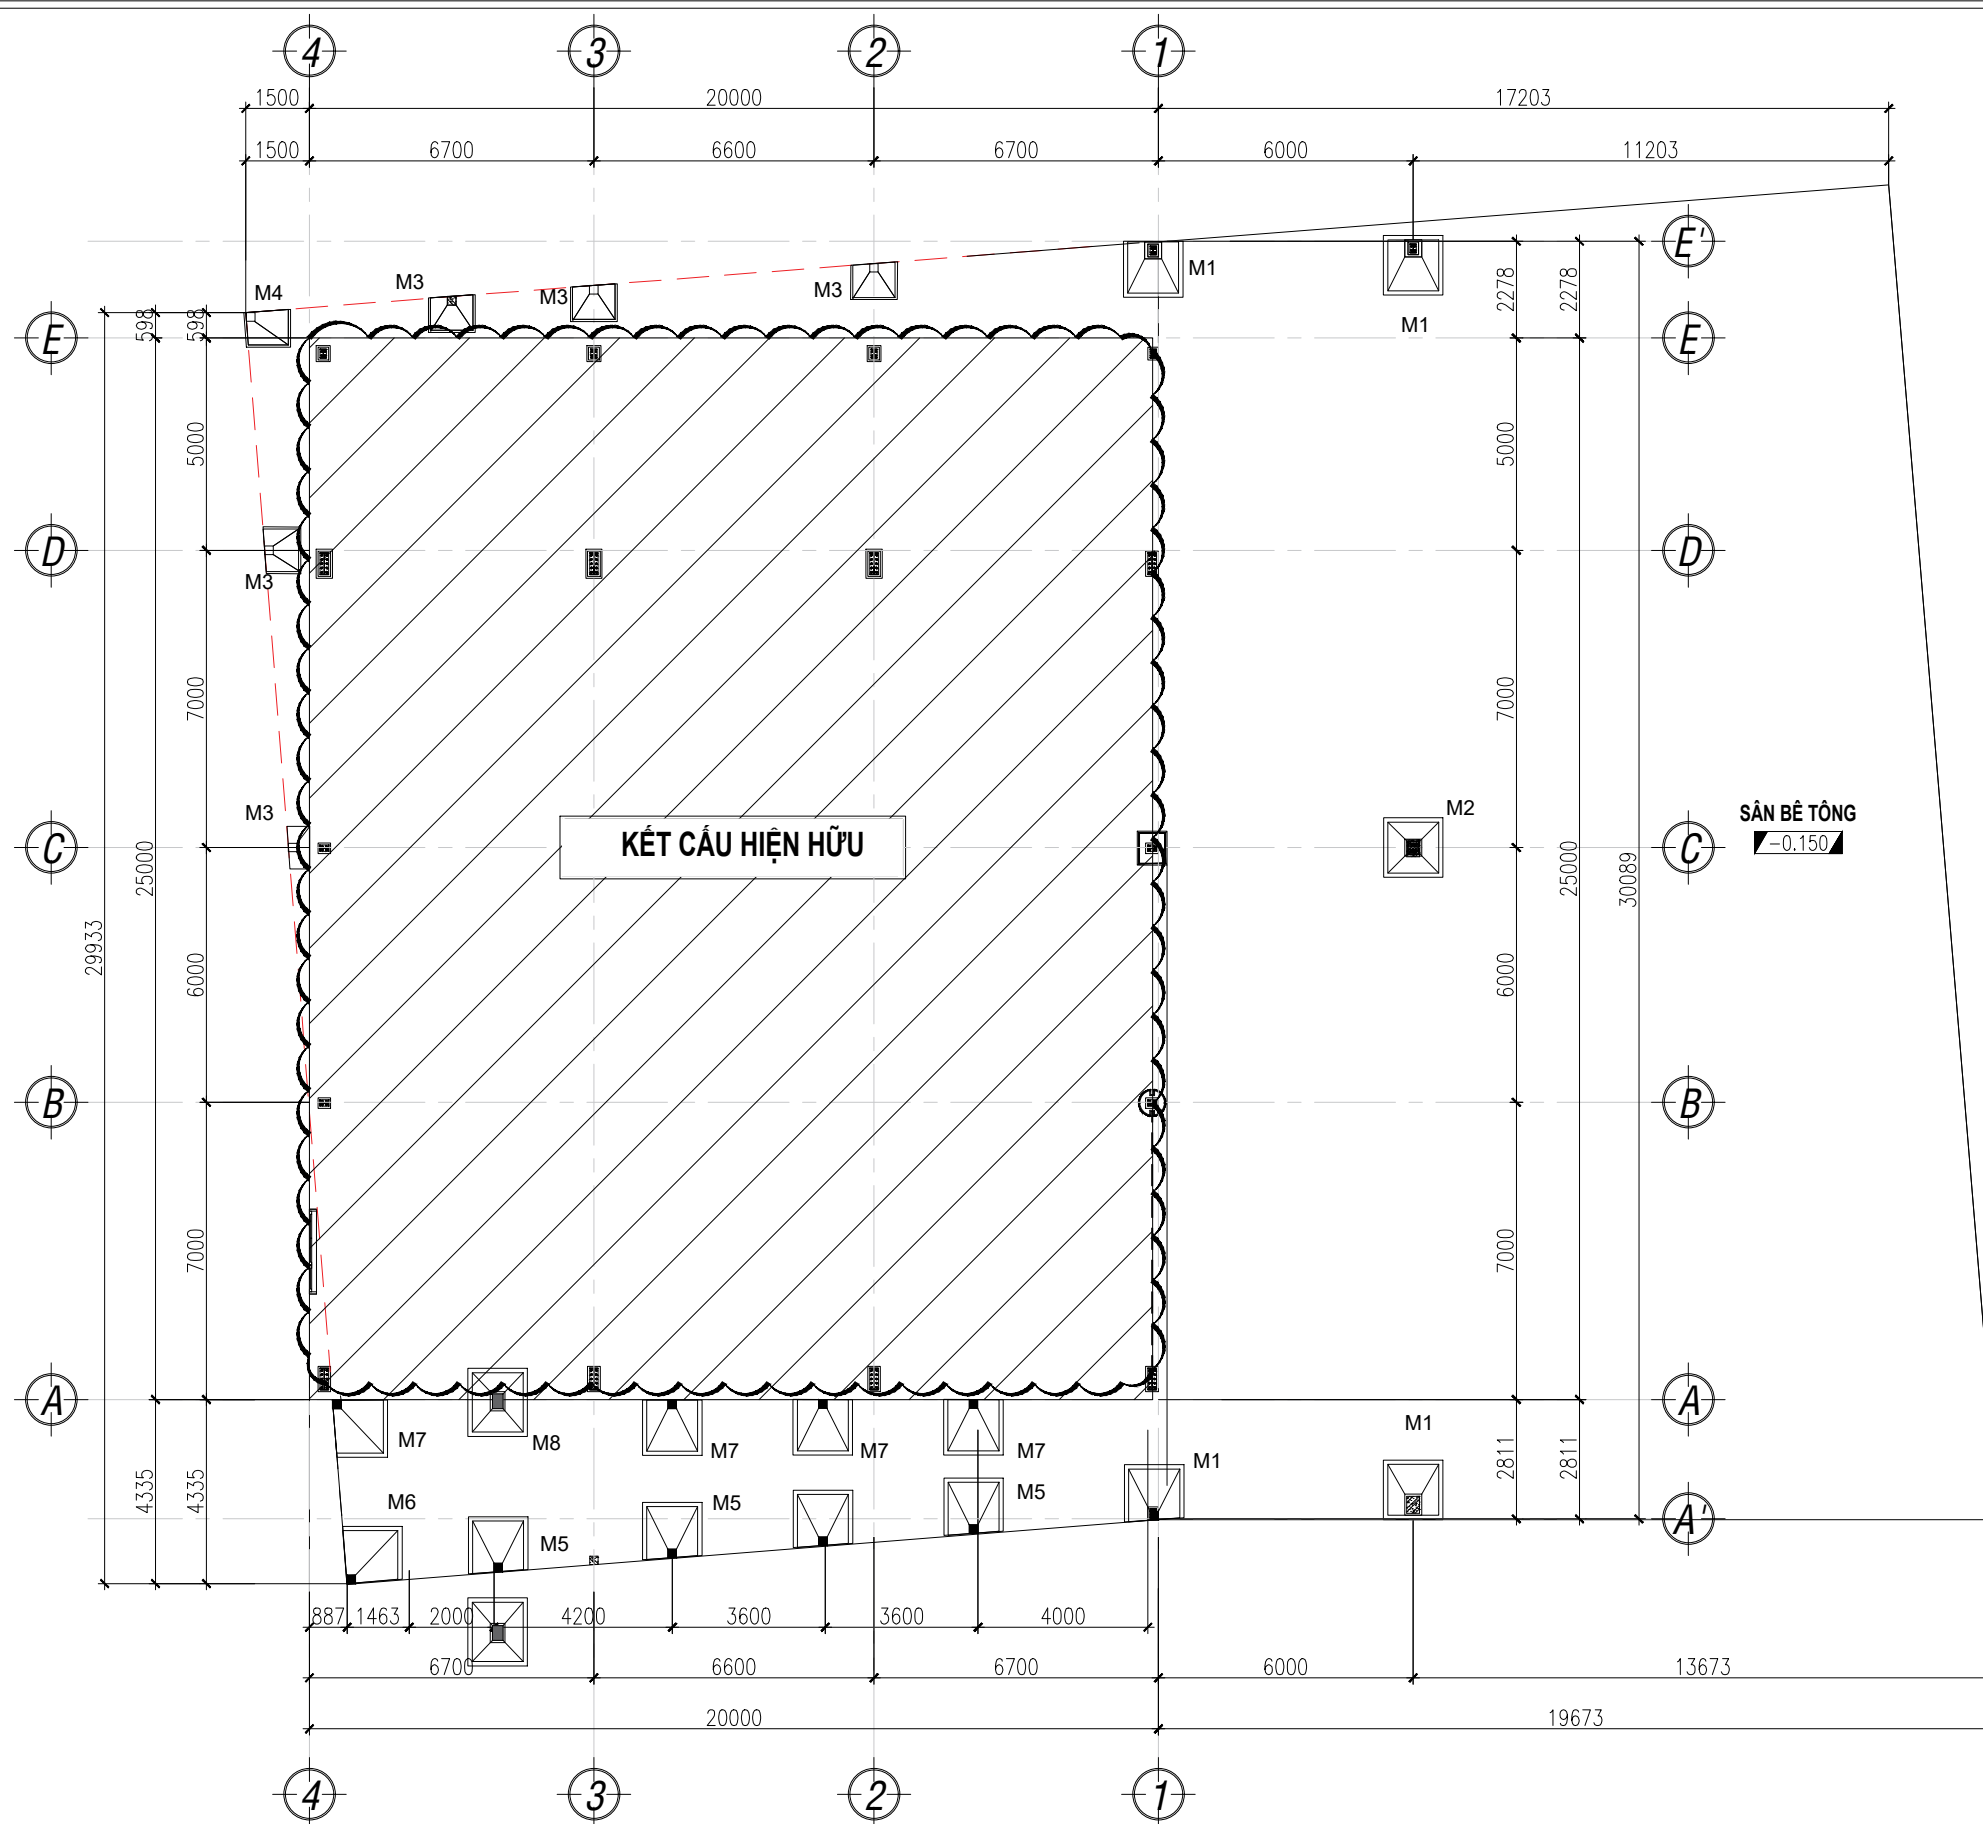

MẶT BẰNG MÓNG NÂNG CẤP
TL: 1/100

HIỆU CHỈNH:

STT	Ngày	Nội dung
01		
02		
03		

CHỦ ĐẦU TƯ

CÔNG TY CỔ PHẦN

TẬP ĐOÀN HOA SEN

ĐỊA CHỈ: 183 NGUYỄN VĂN TRÔI,

PHƯỜNG PHÚ NHUẬN, TP HỒ CHÍ MINH, VIỆT NAM

QUẢN LÝ THIẾT KẾ:

TRẦN DUY PHAN

THIẾT KẾ KIẾN TRÚC:

NGUYỄN VĂN THANH

THIẾT KẾ KẾT CẤU:

PHAN VĂN MINH

THIẾT KẾ CƠ ĐIỆN:

NGUYỄN THANH TÂN

DỰ ÁN

CỬA HÀNG

HOA SEN HOME PHỦ LÝ

ĐỊA CHỈ: TÔ DÂN PHỐ LÃO CẦU, PHƯỜNG HÀ NAM, NINH BÌNH

HẠNG MỤC

KẾT CẤU

TÊN BẢN VẼ


MẶT BẰNG MÓNG NÂNG CẤP

NGÀY IN


SỐ BẢN VẼ

HS.Dw:


Tất cả kích thước, CTKT phải được kiểm tra thực tế tại công trường.

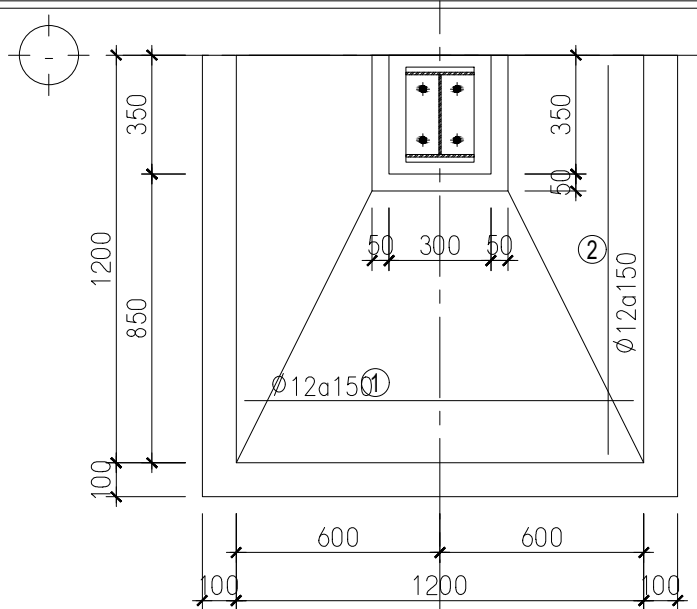


MÔNG M-1

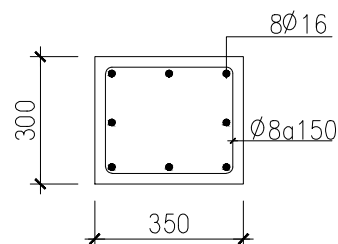


MC 1A-1A

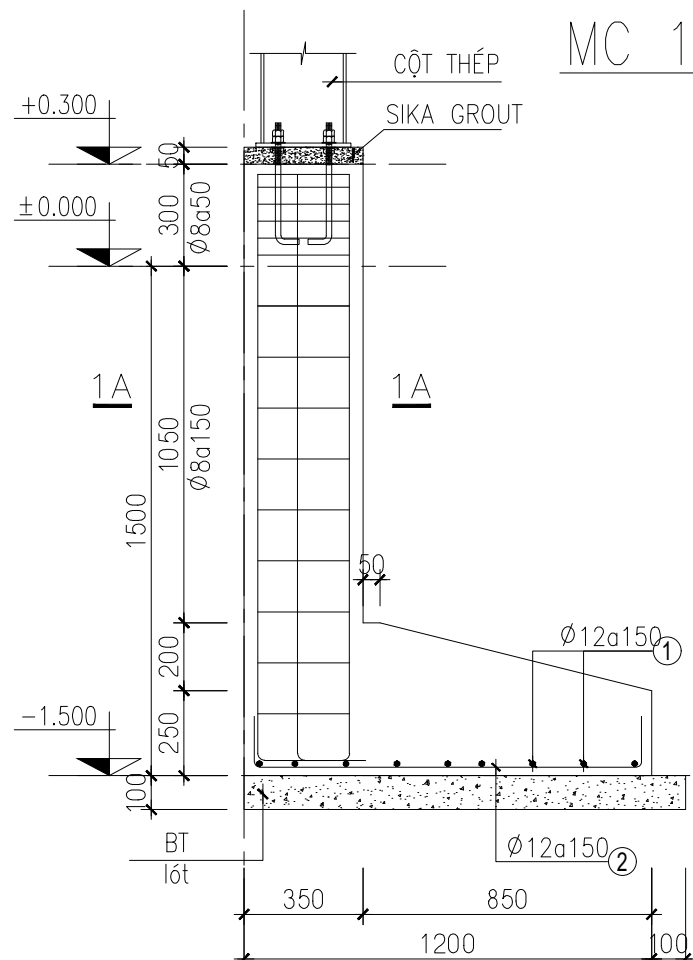


MẶT CẮT 1-1

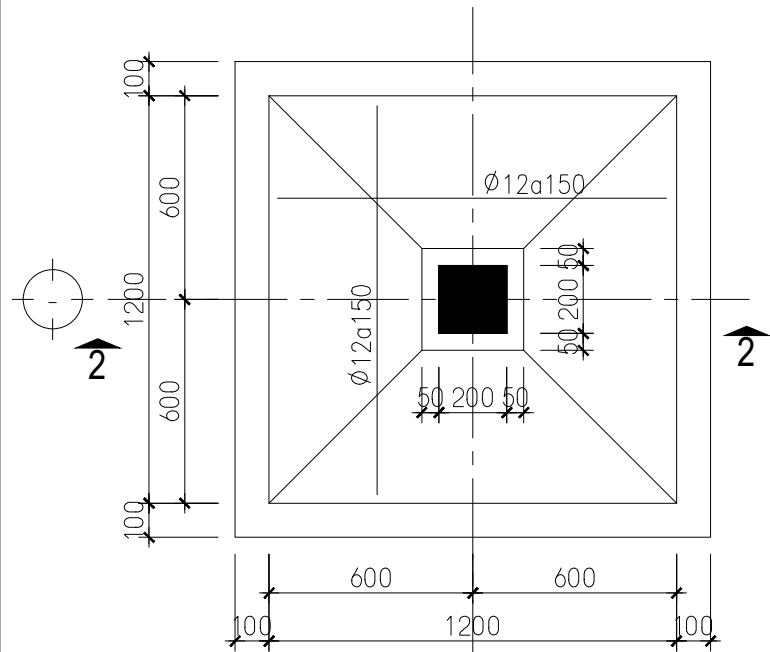

MC 2A-2A

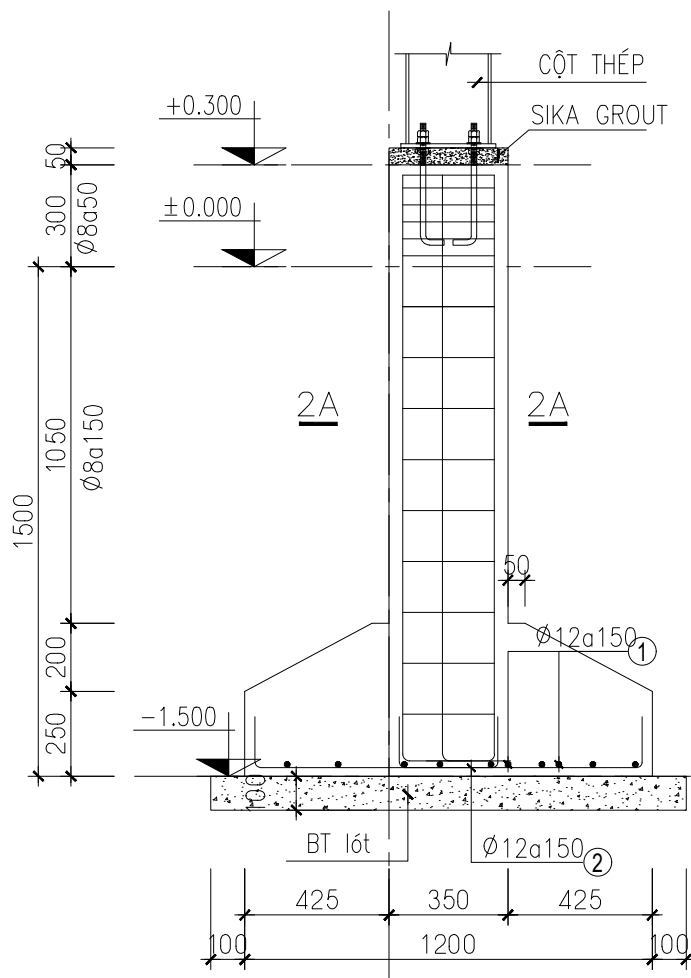


MẶT CẮT 2-2

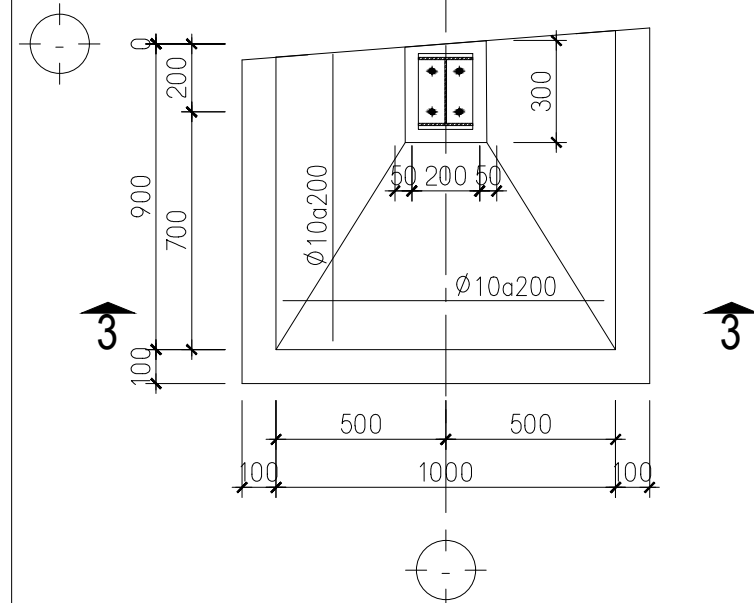


MÔNG M-3

TL 1/25

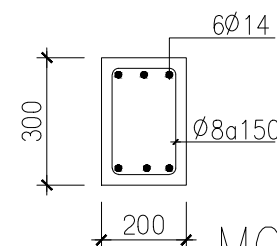

MC 2A-2A

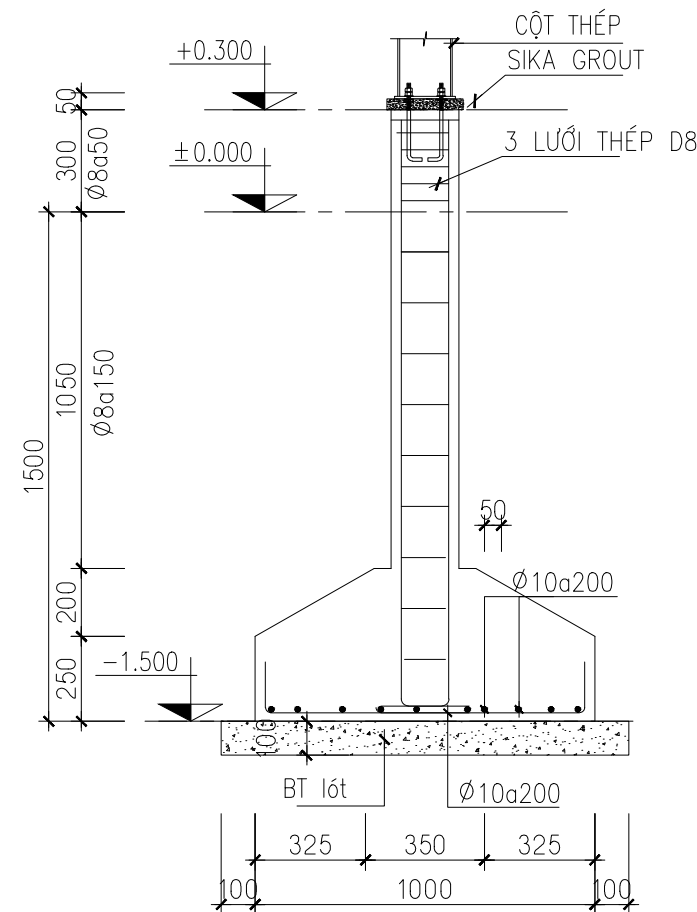

MẶT CẮT 2-2

BẢN VẼ THIẾT KẾ THI CÔNG

HIỆU CHỈNH:		
STT	Ngày	Nội dung
01		
02		
03		




CHỦ ĐẦU TƯ
**CÔNG TY CỔ PHẦN
TẬP ĐOÀN HOA SEN**
ĐỊA CHỈ: 183 NGUYỄN VĂN TRỖI,
PHƯỜNG PHÚ NHUẬN, TP HỒ CHÍ MINH, VIỆT NAM


QUẢN LÝ THIẾT KẾ:	
TRẦN DUY PHAN	
THIẾT KẾ KIẾN TRÚC:	
NGUYỄN VĂN THANH	
THIẾT KẾ KẾT CẤU:	
PHAN VĂN MINH	
THIẾT KẾ CƠ ĐIỆN:	
NGUYỄN THANH TÂN	

DỰ ÁN	
CỬA HÀNG HOA SEN HOME PHỦ LÝ	
ĐỊA CHỈ: TÔ DÂN PHỐ LÃO CẦU, PHƯỜNG HÀ NAM, NINH BÌNH	
HẠNG MỤC	
KẾT CẤU	
TÊN BẢN VẼ	
MẶT BẰNG KẾT CẤU MÔNG	
NGÀY IN	
SỐ BẢN VẼ	
HS.Dw:	


Tất cả kích thước, CTKT phải được kiểm tra thực tế tại công trường.

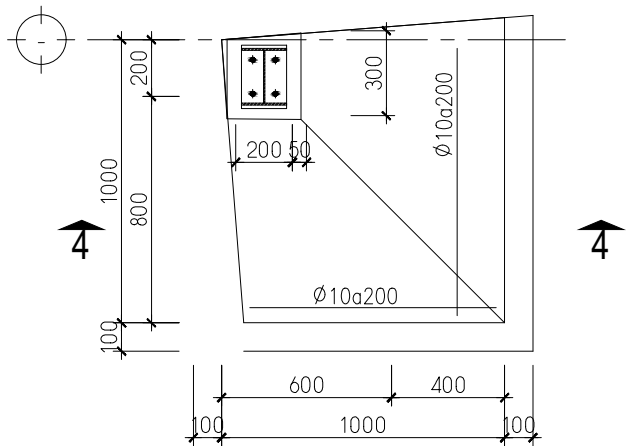


MÓNG M-4
TL 1/25

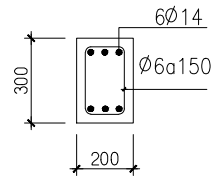


MC 4A-4A
TL 1/25

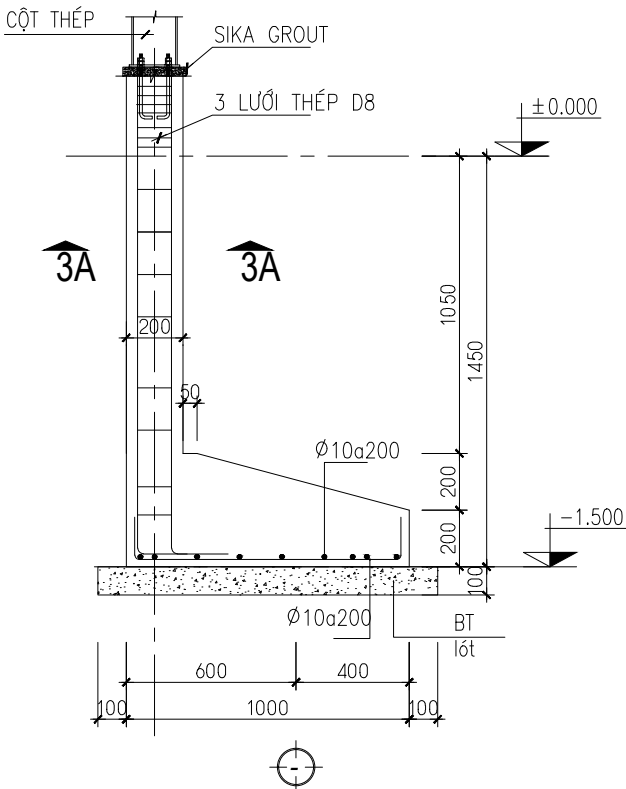


MẶT CẮT 4-4
TL 1/25

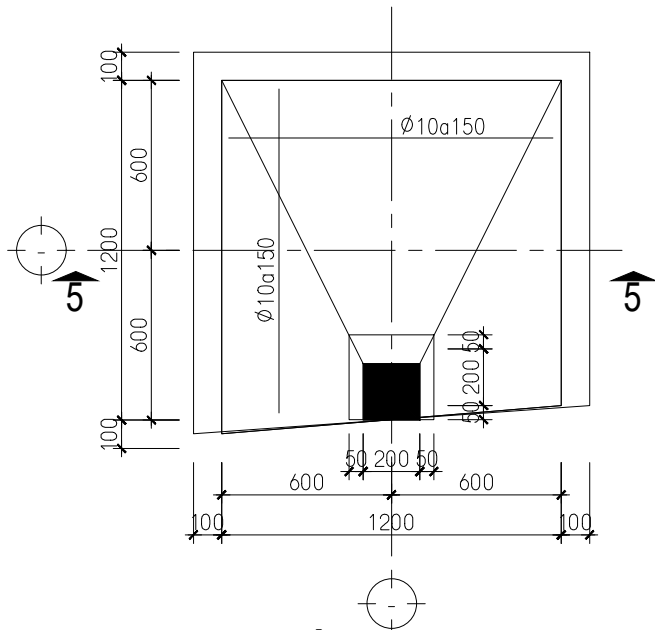


MÓNG M-5
TL 1/25

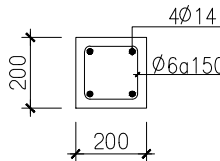


MC 5A-5A
TL 1/25

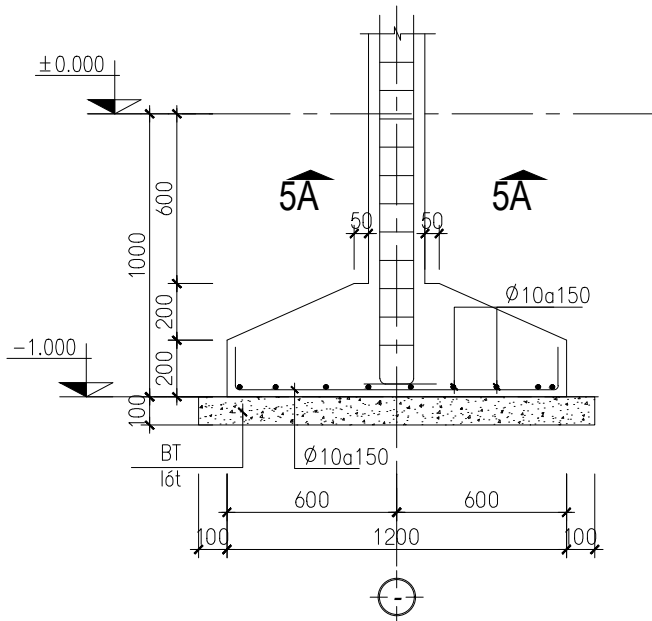


MẶT CẮT 5-5
TL 1/25

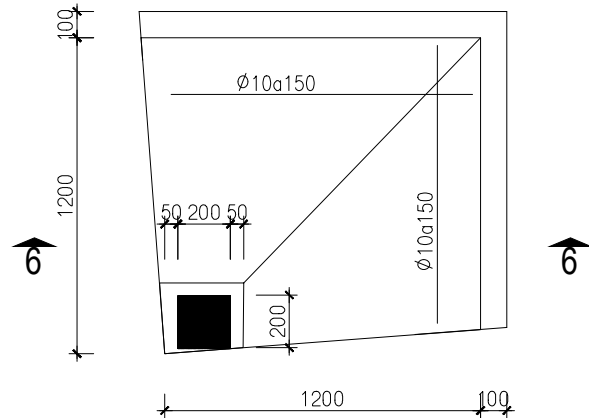

MÓNG M-6
TL 1/25

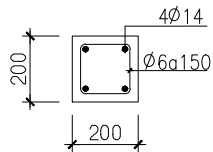

MC 6A-6A
TL 1/25

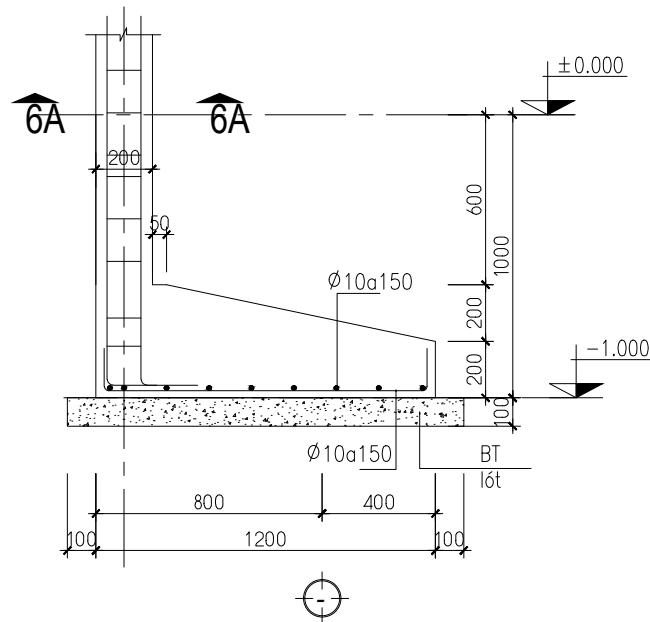

MC 6-6
TL 1/25

BẢN VẼ THIẾT KẾ THI CÔNG

HIỆU CHỈNH:		
STT	Ngày	Nội dung
01		
02		
03		



CHỦ ĐẦU TƯ
**CÔNG TY CỔ PHẦN
TẬP ĐOÀN HOA SEN**
ĐỊA CHỈ: 183 NGUYỄN VĂN TRỖI,
PHƯỜNG PHÚ NHUẬN, TP HỒ CHÍ MINH, VIỆT NAM

QUẢN LÝ THIẾT KẾ:

TRẦN DUY PHAN

THIẾT KẾ KIẾN TRÚC:

NGUYỄN VĂN THANH

THIẾT KẾ KẾT CẤU:

PHAN VĂN MINH

THIẾT KẾ CƠ ĐIỆN:

NGUYỄN THANH TÂN

DỰ ÁN

**CỬA HÀNG
HOA SEN HOME PHỦ LÝ**

ĐỊA CHỈ: TÔ DÂN PHỐ LÃO CẦU, PHƯỜNG HÀ NAM, NINH BÌNH

HẠNG MỤC

KẾT CẤU

TÊN BẢN VẼ


CHI TIẾT KẾT CẤU MÓNG

NGÀY IN

SỐ BẢN VẼ


HS.Dw:

Tất cả kích thước, CTKT phải được kiểm tra thực tế tại công trường.

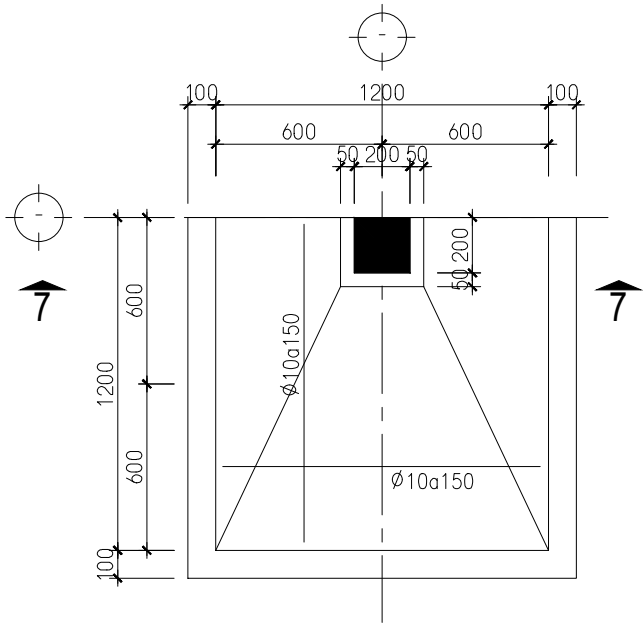


MÓNG M-7

TL 1/25

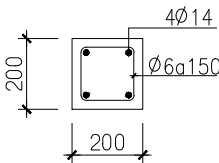


MC 7A-7A

TL 1/25

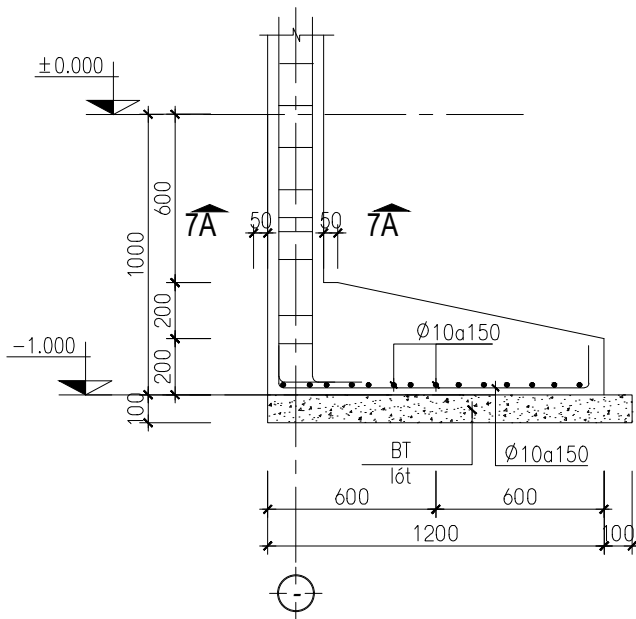


MẶT CẮT 7-7


TL 1/25

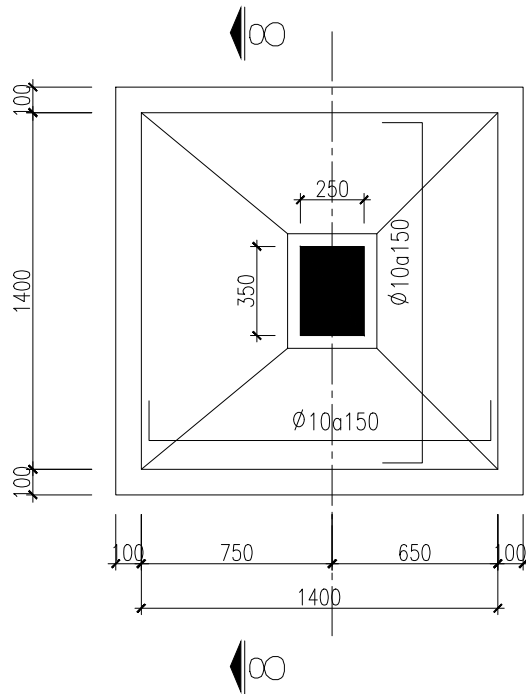


CHI TIẾT MÓNG M8

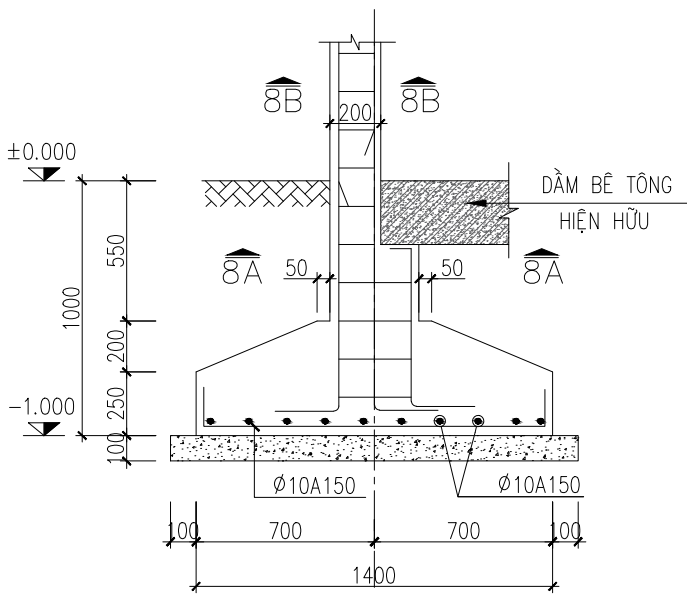


MẶT CẮT 8-8

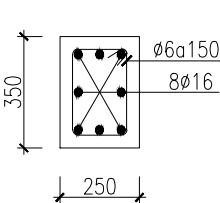

MẶT CẮT 8A-8A

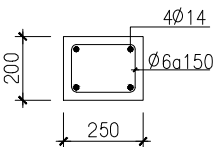

MẶT CẮT 8B-8B

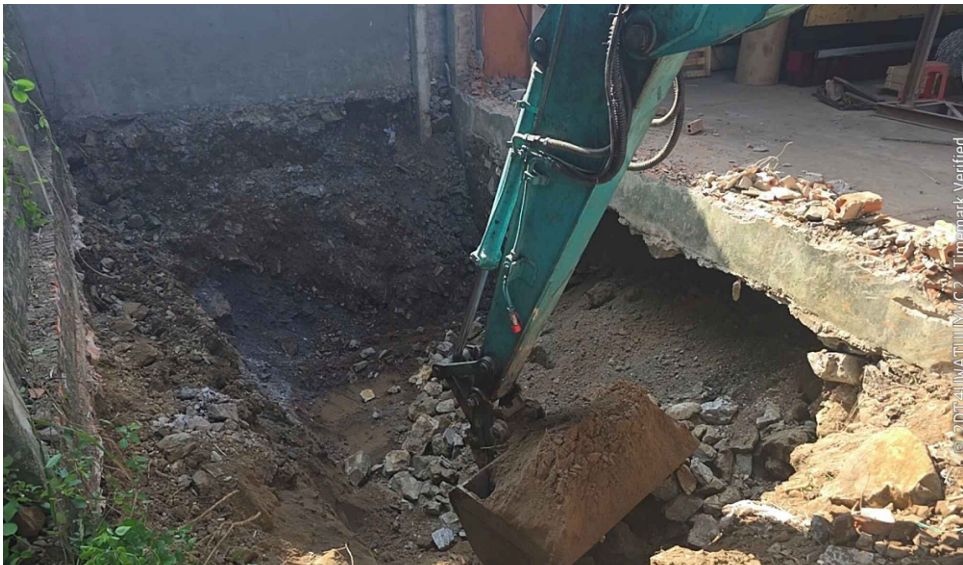

– PHẦN HỎ HÀM ẾCH ĐỔ BÙ BẰNG BÊ TÔNG LÓT M100. ĐÁ 1X2

BẢN VẼ THIẾT KẾ THI CÔNG

HIỆU CHỈNH:		
STT	Ngày	Nội dung
01		
02		
03		



CHỦ ĐẦU TƯ
CÔNG TY CỔ PHẦN
TẬP ĐOÀN HOA SEN
ĐỊA CHỈ: 183 NGUYỄN VĂN TRỖI,
PHƯỜNG PHÚ NHUẬN, TP HỒ CHÍ MINH, VIỆT NAM



QUẢN LÝ THIẾT KẾ:	
TRẦN DUY PHAN	
THIẾT KẾ KIẾN TRÚC:	
NGUYỄN VĂN THANH	
THIẾT KẾ KẾT CẤU:	
PHAN VĂN MINH	
THIẾT KẾ CƠ ĐIỆN:	
NGUYỄN THANH TÂN	

DỰ ÁN
CỬA HÀNG HOA SEN HOME PHỦ LÝ
ĐỊA CHỈ: TÔ DÂN PHỐ LÃO CẦU, PHƯỜNG HÀ NAM, NINH BÌNH
HẠNG MỤC
KẾT CẤU
TÊN BẢN VẼ
CHI TIẾT KẾT CẤU MÓNG
NGÀY IN
SỐ BẢN VẼ
HS.Dw:

Tất cả kích thước, CTKT phải được kiểm tra thực tế tại công trường.


MẶT BẰNG
ĐÀ KIỀNG
TL: 1/100

CT KHOAN CÂY THÉP

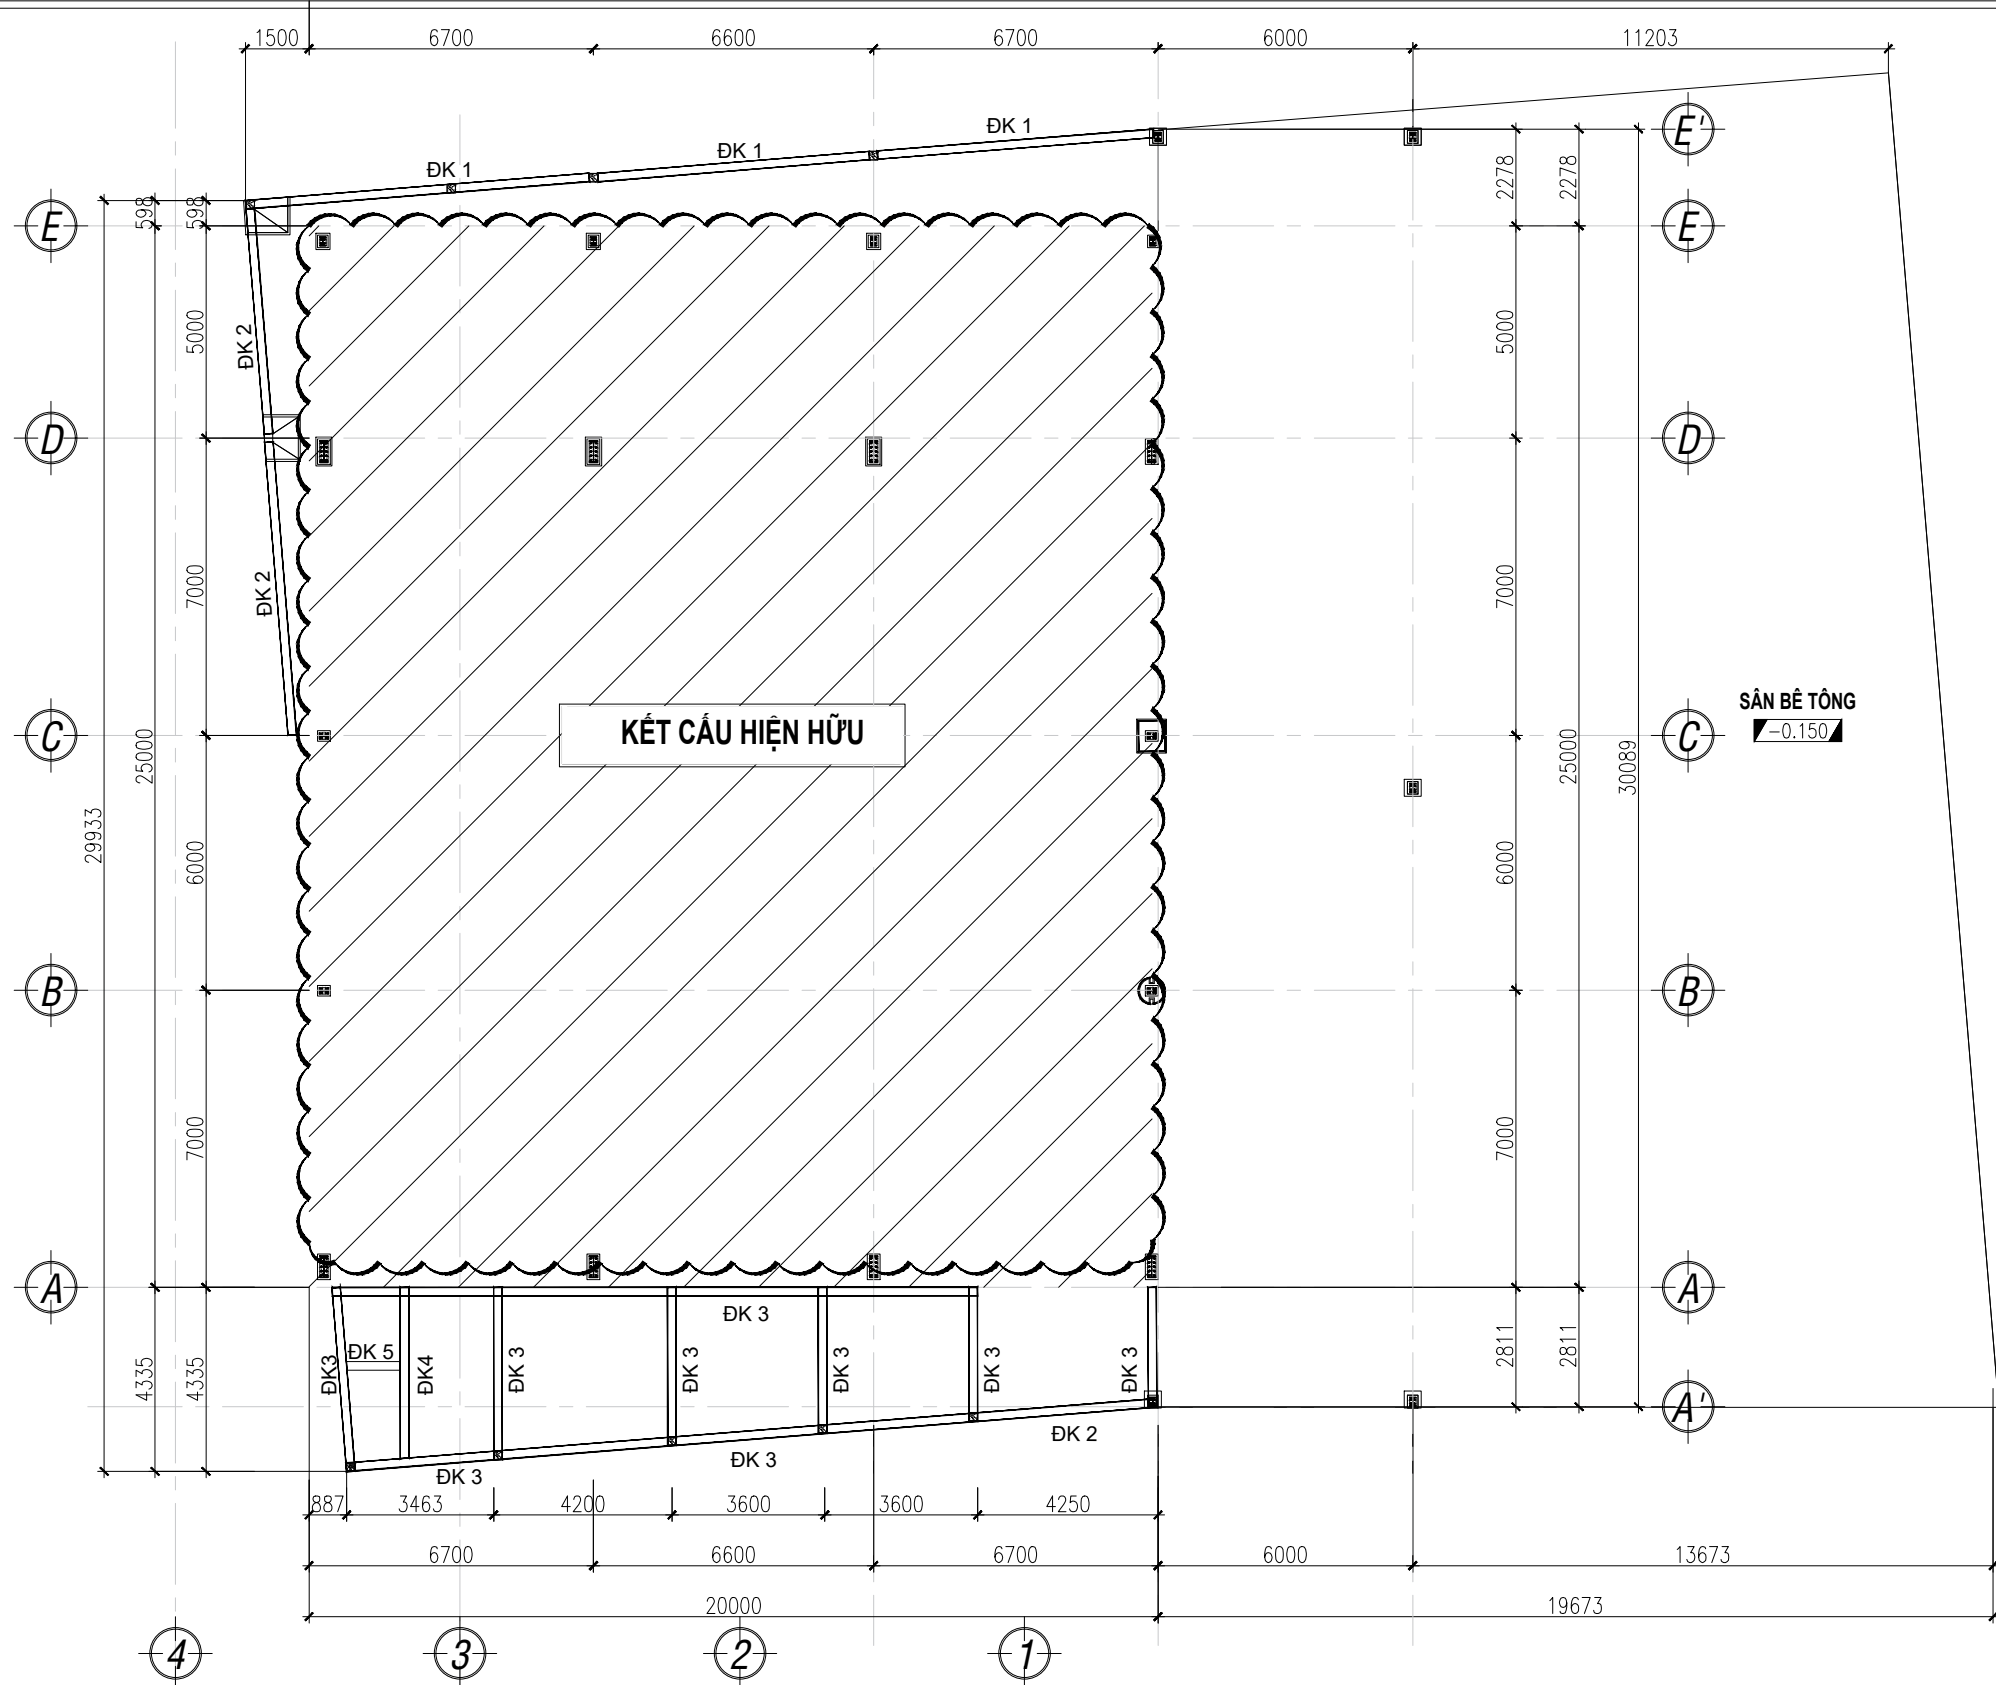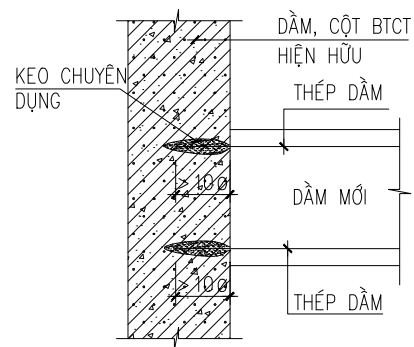


ĐÀ KIỀNG ĐK-1


TL 1/25

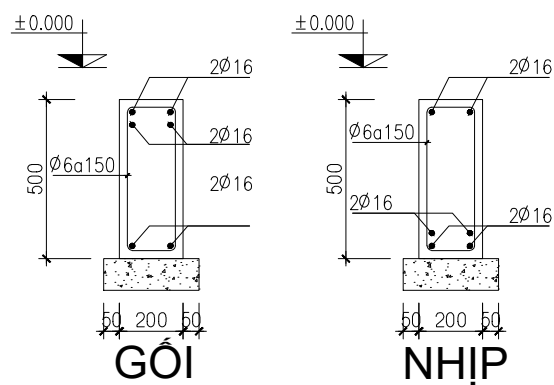


ĐÀ KIỀNG ĐK-2
TL 1/25

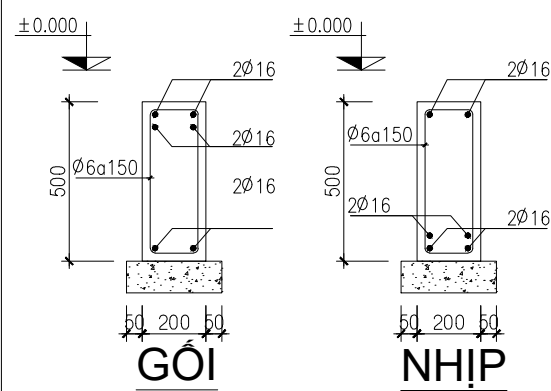


ĐÀ KIỀNG ĐK-3
TL 1/25

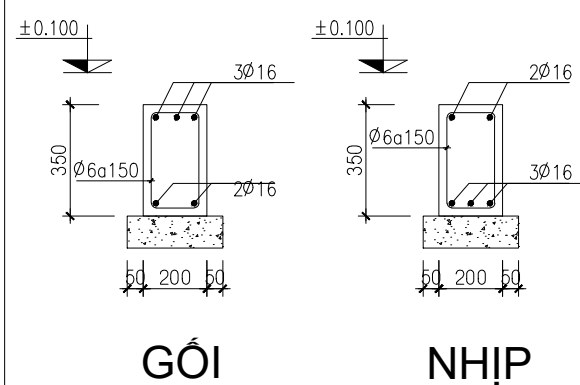

ĐÀ KIỀNG ĐK-4
TL 1/25

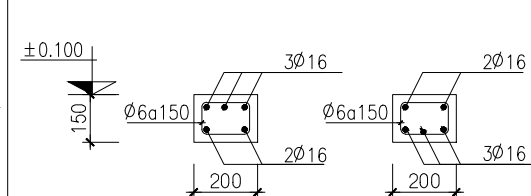

ĐÀ KIỀNG ĐK-5
TL 1/25

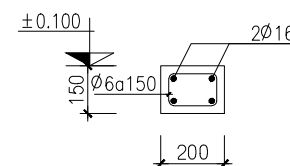

BẢN VẼ THIẾT KẾ THI CÔNG

HIỆU CHỈNH:

STT	Ngày	Nội dung
01		
02		
03		



CHỦ ĐẦU TƯ
CÔNG TY CỔ PHẦN
TẬP ĐOÀN HOA SEN
ĐỊA CHỈ: 183 NGUYỄN VĂN TRÔI,
PHƯỜNG PHÚ NHUẬN, TP HỒ CHÍ MINH, VIỆT NAM

QUẢN LÝ THIẾT KẾ:

TRẦN DUY PHAN

THIẾT KẾ KIẾN TRÚC:

NGUYỄN VĂN THANH

THIẾT KẾ KẾT CẤU:

PHAN VĂN MINH

THIẾT KẾ CƠ ĐIỆN:

NGUYỄN THANH TÂN.....

DỰ ÁN

CỬA HÀNG
HOA SEN HOME PHỦ LÝ

ĐỊA CHỈ: TỔ DÂN PHỐ LÃO CẦU, PHƯỜNG HÀ NAM, NINH BÌNH

HẠNG MỤC

KẾT CẤU

TÊN BẢN VẼ


MẶT BẰNG MÓNG NÂNG CẤP

NGÀY IN


SỐ BẢN VẼ

HS.Dw:


Tất cả kích thước, CTKT phải được kiểm tra thực tế tại công trường.

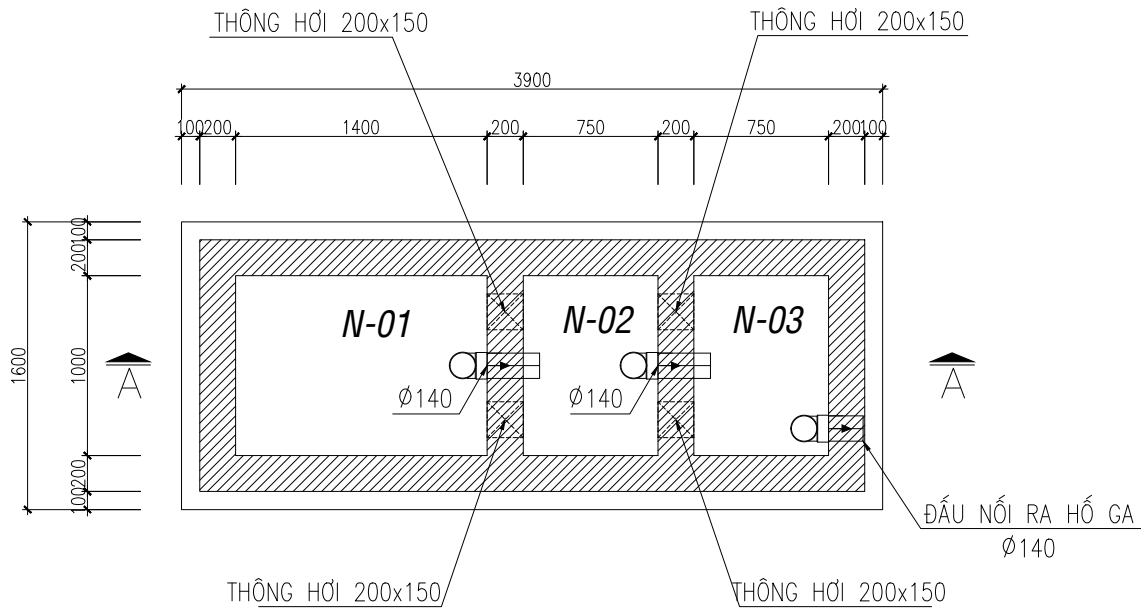


MẶT BẰNG BỂ TỰ HOẠI

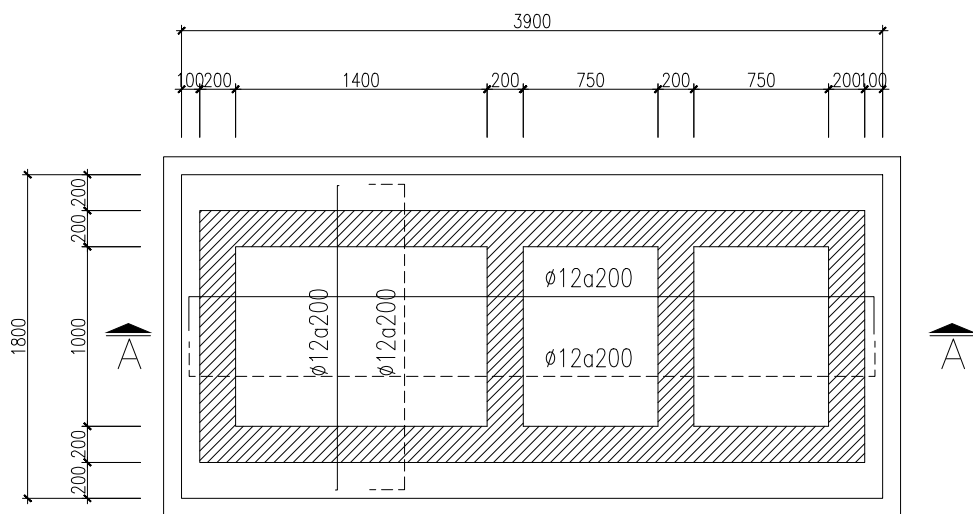


MẶT BẰNG BỐ TRÍ THÉP BẢN ĐÁY

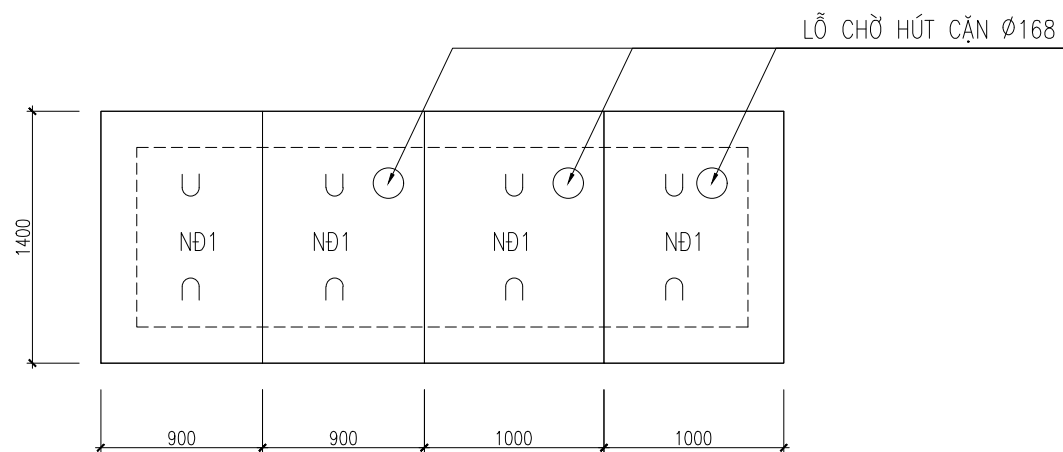


MẶT BẰNG NẮP ĐÀN

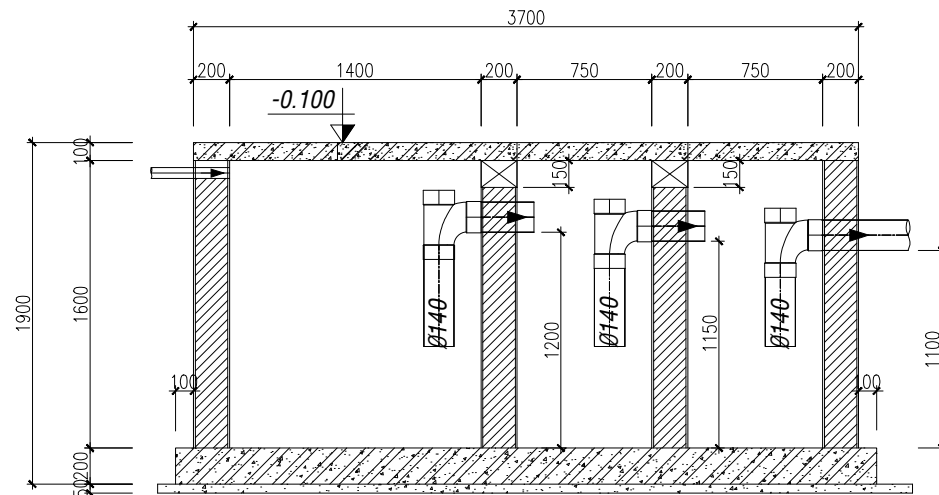


MẶT CẮT A-A

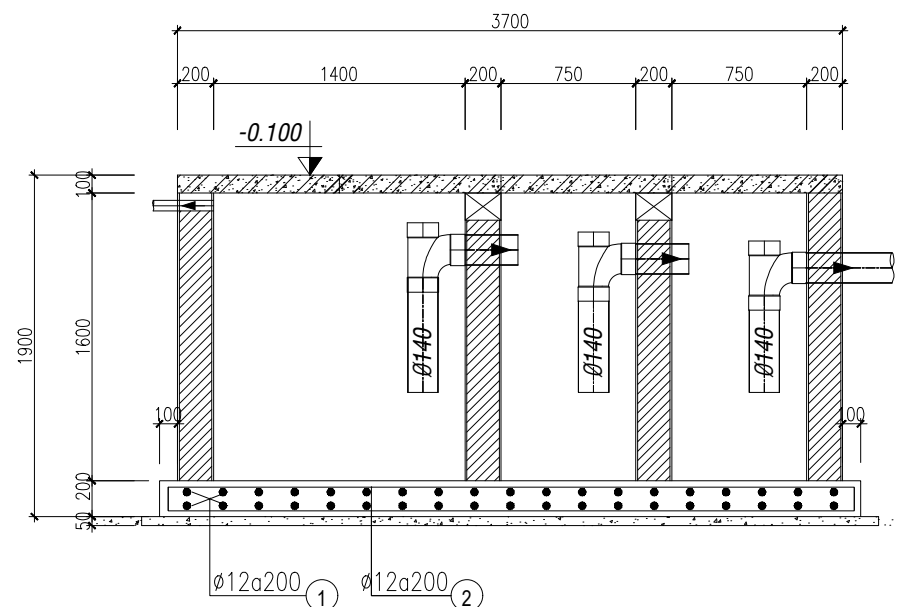

MẶT CẮT A-A BỐ TRÍ THÉP

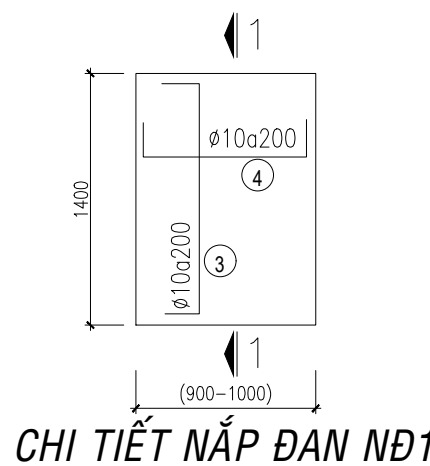

CHI TIẾT NẮP ĐÀN NĐ1

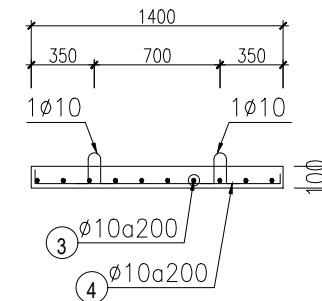

MẶT CẮT 1-1

- * GHI CHÚ :
- TƯỜNG XÂY GẠCH ĐẶC, VỮA XÂY MẮC 75
 - TƯỜNG TRÁT 2 LỚP VỮA MẮC 75
 - ĐÓNG LƯỚI THÉP (RỘNG 300 mm) TẠI CÁC VỊ TRÍ TIẾP GIÁP TƯỜNG VÀ SÀN ĐÁY

BẢN VẼ THIẾT KẾ THI CÔNG

HIỆU CHỈNH:		
STT	Ngày	Nội dung
01		
02		
03		



CHỦ ĐẦU TƯ
**CÔNG TY CỔ PHẦN
TẬP ĐOÀN HOA SEN**
ĐỊA CHỈ: 183 NGUYỄN VĂN TRỖI,
PHƯỜNG PHÚ NHUẬN, TP HỒ CHÍ MINH, VIỆT NAM

QUẢN LÝ THIẾT KẾ:	
TRẦN DUY PHAN	
THIẾT KẾ KIẾN TRÚC:	
NGUYỄN VĂN THANH	
THIẾT KẾ KẾT CẤU:	
PHAN VĂN MINH	
THIẾT KẾ CƠ ĐIỆN:	
NGUYỄN THANH TÂN	

DỰ ÁN
CỬA HÀNG HOA SEN HOME PHỦ LÝ
ĐỊA CHỈ: TÔ DÂN PHỐ LÃO CẦU, PHƯỜNG HÀ NAM, NINH BÌNH
HẠNG MỤC
KẾT CẤU
TÊN BẢN VẼ
CHI TIẾT BỂ TỰ HOẠI
NGÀY IN
SỐ BẢN VẼ
HS.Dw: KC-49

Tất cả kích thước, CTKT phải được kiểm tra thực tế tại công trường.